


BESCHREIBUNG

Übersicht schräg von oben: Bestand auf Flst. 121/1, Neubau Bungalow V1 auf Flst. 121/2.

PROJEKT		FLURSTÜCKE
Ashausener Str. 12, Stelle		Flst. 121/1 + 121/2
ANSICHT		VARIANTE
01 Luftansicht		Bungalow V1, Lage Ost
DATUM	BLATT	STATUS
15.10.2026	1/5	**VORENTWURF, keine Bauvorlage**

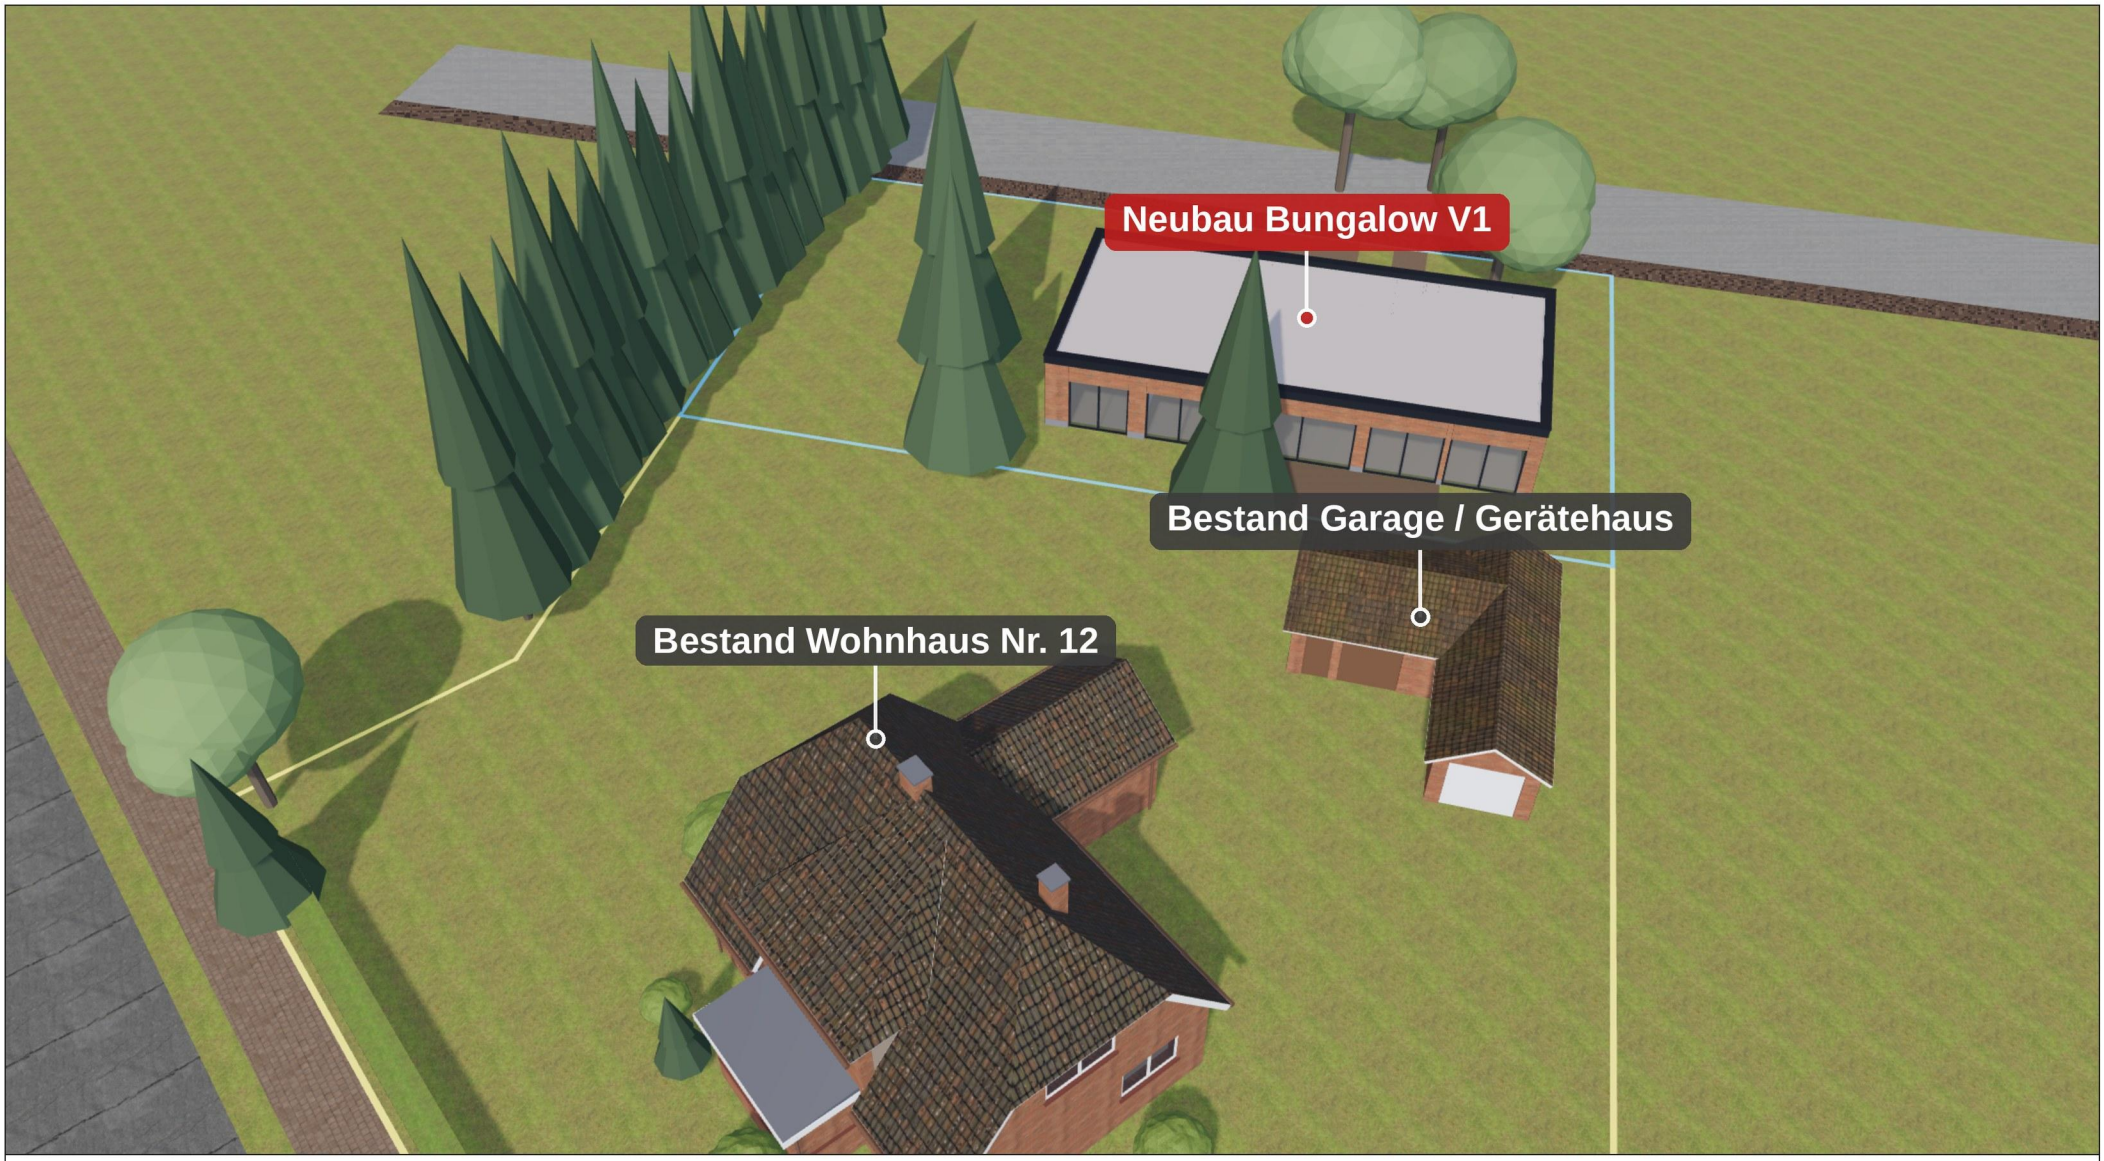

BESCHREIBUNG

Blick von der Straße Am Osterfeld auf die Nordseite des Bungalows.

PROJEKT		FLURSTÜCKE
Ashausener Str. 12, Stelle		Flst. 121/1 + 121/2
ANSICHT		VARIANTE
02 Straßenansicht		Bungalow V1, Lage Ost
DATUM	BLATT	STATUS
15.10.2026	2/5	**VORENTWURF, keine Bauvorlage**



BESCHREIBUNG

Blick von Flst. 121/1 auf die Gartenseite des Bungalows, rechts Gerätehaus / Garage.

PROJEKT		FLURSTÜCKE
Ashausener Str. 12, Stelle		Flst. 121/1 + 121/2
ANSICHT		VARIANTE
03 Gartenansicht		Bungalow V1, Lage Ost
DATUM	BLATT	STATUS
15.10.2026	3/5	**VORENTWURF, keine Bauvorlage**



BESCHREIBUNG

Blick aus dem Wohnzimmer des Bungalows durch die Verglasung Richtung Bestandshaus.

PROJEKT		FLURSTÜCKE
Ashausener Str. 12, Stelle		Flst. 121/1 + 121/2
ANSICHT		VARIANTE
04 Innenansicht		Bungalow V1, Lage Ost
DATUM	BLATT	STATUS
15.10.2026	4/5	**VORENTWURF, keine Bauvorlage**



GRZ-Nachweis

Grundstücksfläche Flst. 121/2	**701 m²**
zulässige Grundfläche (GRZ 0,25)	**175,3 m²**
geplante Grundfläche Bungalow V1	**174,8 m²** ✓

Abstandsflächen (mind. 3,00 m)

LAGE	SÜD	NORD	WEST	OST	
Ost (V1)	3,03 m	7,02 m	14,34 m	3,04 m	✓
Mitte	3,03 m	7,02 m	8,64 m	8,74 m	✓
West	3,03 m	7,02 m	3,07 m	14,31 m	✓

Alle drei Lagen eingehalten (Grundfläche und Abstände).
Annahmen: 121/2 eigenes Baugrundstück, GRZ 0,25 lt. B-Plan 32/50 (BauNVO 1977, § 19 Abs. 4: Terrasse/Stellplätze nicht angerechnet); NBauO § 5: 0,5 H, mind. 3 m; H = 3,40 m. Maße aus Lageplan, ±0,25 m.

Legende: rot gefüllt = Lage Ost (V1) · rot gestrichelt = Lage Mitte / West · hellrot schraffiert = Abstandsflächen Lage Ost · grau = Bestand

Vorprüfung, ersetzt keine Bauvorlage/Prüfung durch Entwurfsverfasser.

BESCHREIBUNG

Drei mögliche Bungalow-Lagen auf Flst. 121/2, Abstandsflächen der Lage Ost.

PROJEKT	FLURSTÜCKE
Ashausener Str. 12, Stelle	Flst. 121/1 + 121/2
ANSICHT	**VARIANTE**
05 Lageplan 1:500	Bungalow V1, Lagen Ost/Mitte/West
DATUM	**BLATT**	**STATUS**
15.10.2026	5/5	**VORENTWURF, keine Bauvorlage**