

Ashausener Straße 12, 21435 Stelle – Bestand + Neubau Bungalow V1 „0.1.5 kompakt“ auf Flst. 121/2


Vorentwurf / Machbarkeit, keine Bauvorlage · Stand 07.10.2026 · Grundlage: Lageplan LGLN 28.01.2026 (Grenzen ±0,25 m), B-Plan 32/50 „Osterfeld West“, Raumteilung nach T. Oberhofer „_Neubau 0.1.5“

Lageplan Gesamtgrundstück Flst. 121/1 (Bestand) + 121/2 (Neubau) · M 1:400 (bei A3)



Grundriss Neubau Bungalow V1 · M 1:100 (bei A3)

Raumteilung nach Oberhofer „_Neubau 0.1.5“, auf 40 cm Außenwände umgerechnet · Flächen ca. (lichte Rechteckmaße)

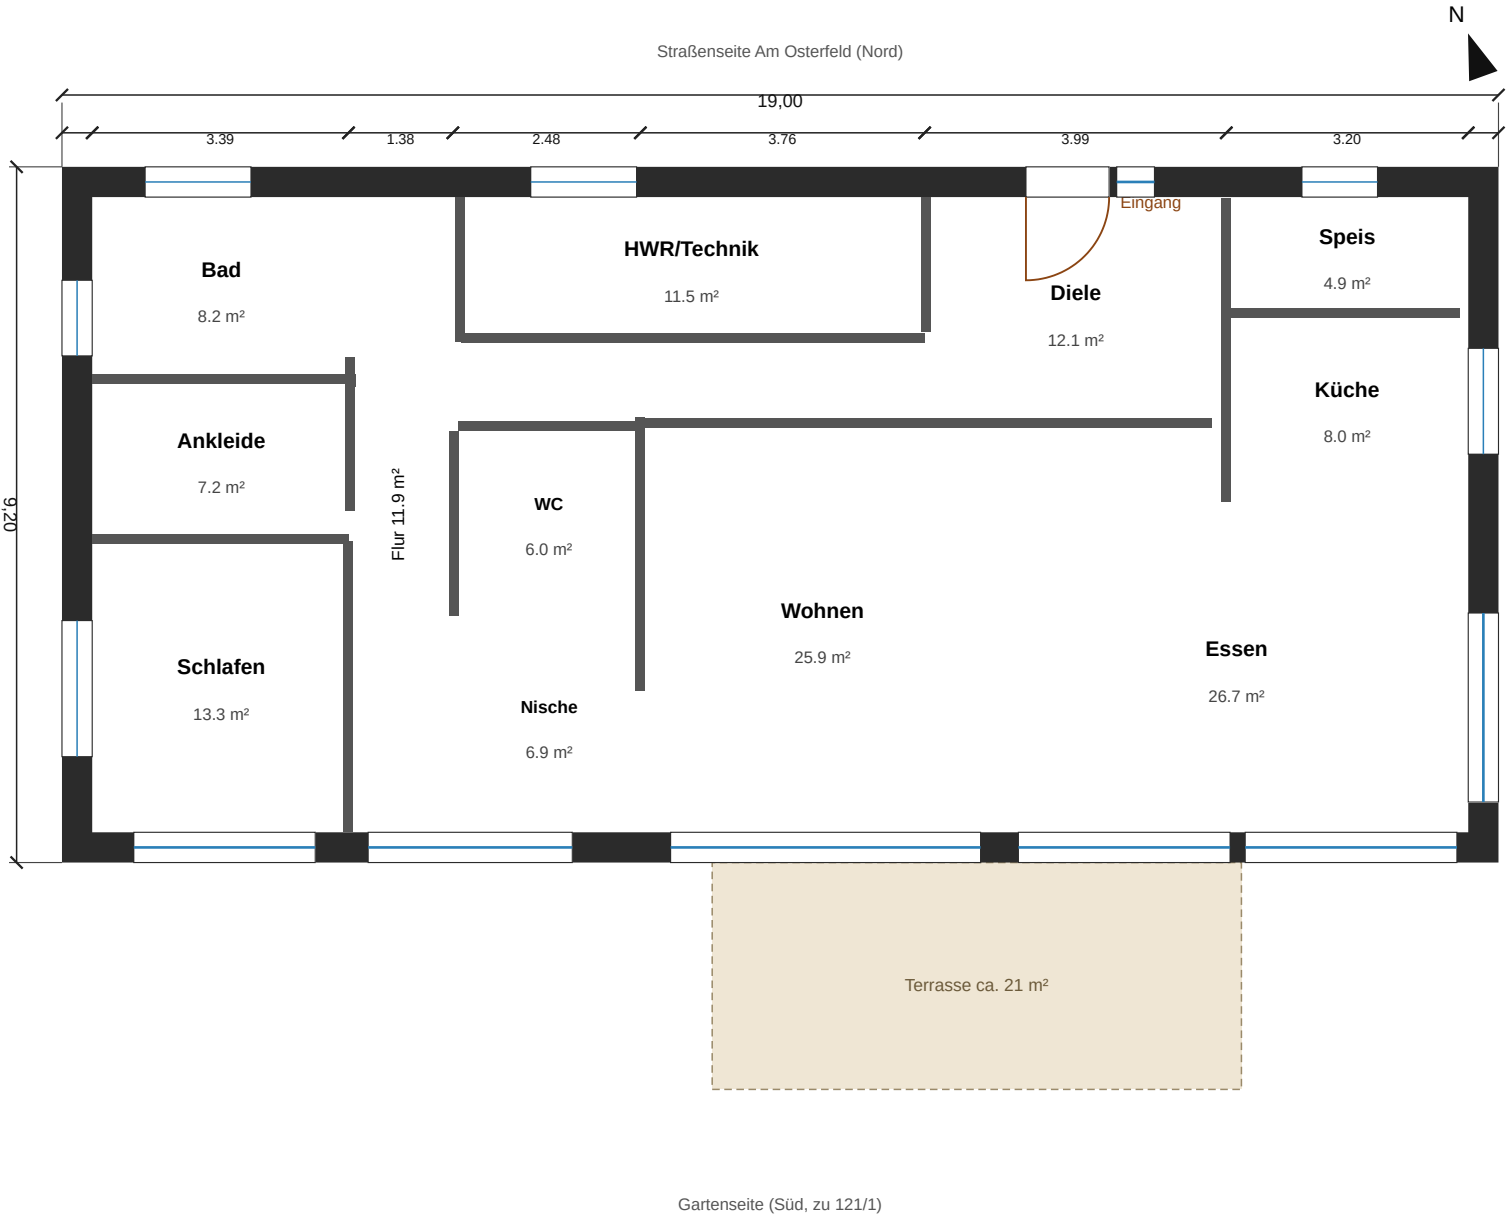

- Bestand (bleibt): Wohnhaus, Garage/Lager, Gerätehaus
- Neubau Bungalow V1, eingeschossig, Flachdach, H ≈ 3,40 m
- Abstandsfläche NBauO § 5: 0,4 H = 1,36 m → mind. 3,00 m
- Terrasse 7,0 × 3,0 m (ebenerdig)
- 2 Stellplätze 5,5 × 5,3 m + Zuweg 1,5 m von Am Osterfeld
- Baugrenze B-Plan 32/50: 7 m Am Osterfeld, 3 m seitlich, 0 m zu 121/1
- Baum/Strauch erhalten (Lage aus Luftbild, ±1 m)
- Fällung: 2 Nadelbäume (17 m, 15 m), 1 Obstbaum (7 m)

Nachweis GR / Abstandsflächen (Annahme: 121/2 eigenes Baugrundstück)

Grundflächenzahl (B-Plan 32/50, WA I)	GRZ 0,25
Flst. 121/2 (ALKIS)	702 m² → zulässige GR 175,5 m²
GR Neubau Bungalow V1: 19,00 × 9,20 m	174,8 m² ≤ 175,5 m² ✓ (Reserve 0,7 m²)
Terrasse 21 m², Stellplätze 29 m², Zuweg 10,5 m²	nach § 19 (4) BauNVO 1977 nicht angerechnet
Gegenprobe BauNVO 1990 (GRZ II, +50 %)	174,8 + 60,5 = 235,3 m² ≤ 263,3 m² ✓
GFZ 0,25 (1 Vollgeschoss, Flachdach)	GF 174,8 m² ≤ 175,5 m² ✓
Abstände zu Grenzen 121/2 (S / N / W / O)	3,03 / 7,03 / 14,40 / 3,03 m ≥ 3,00 m ✓